


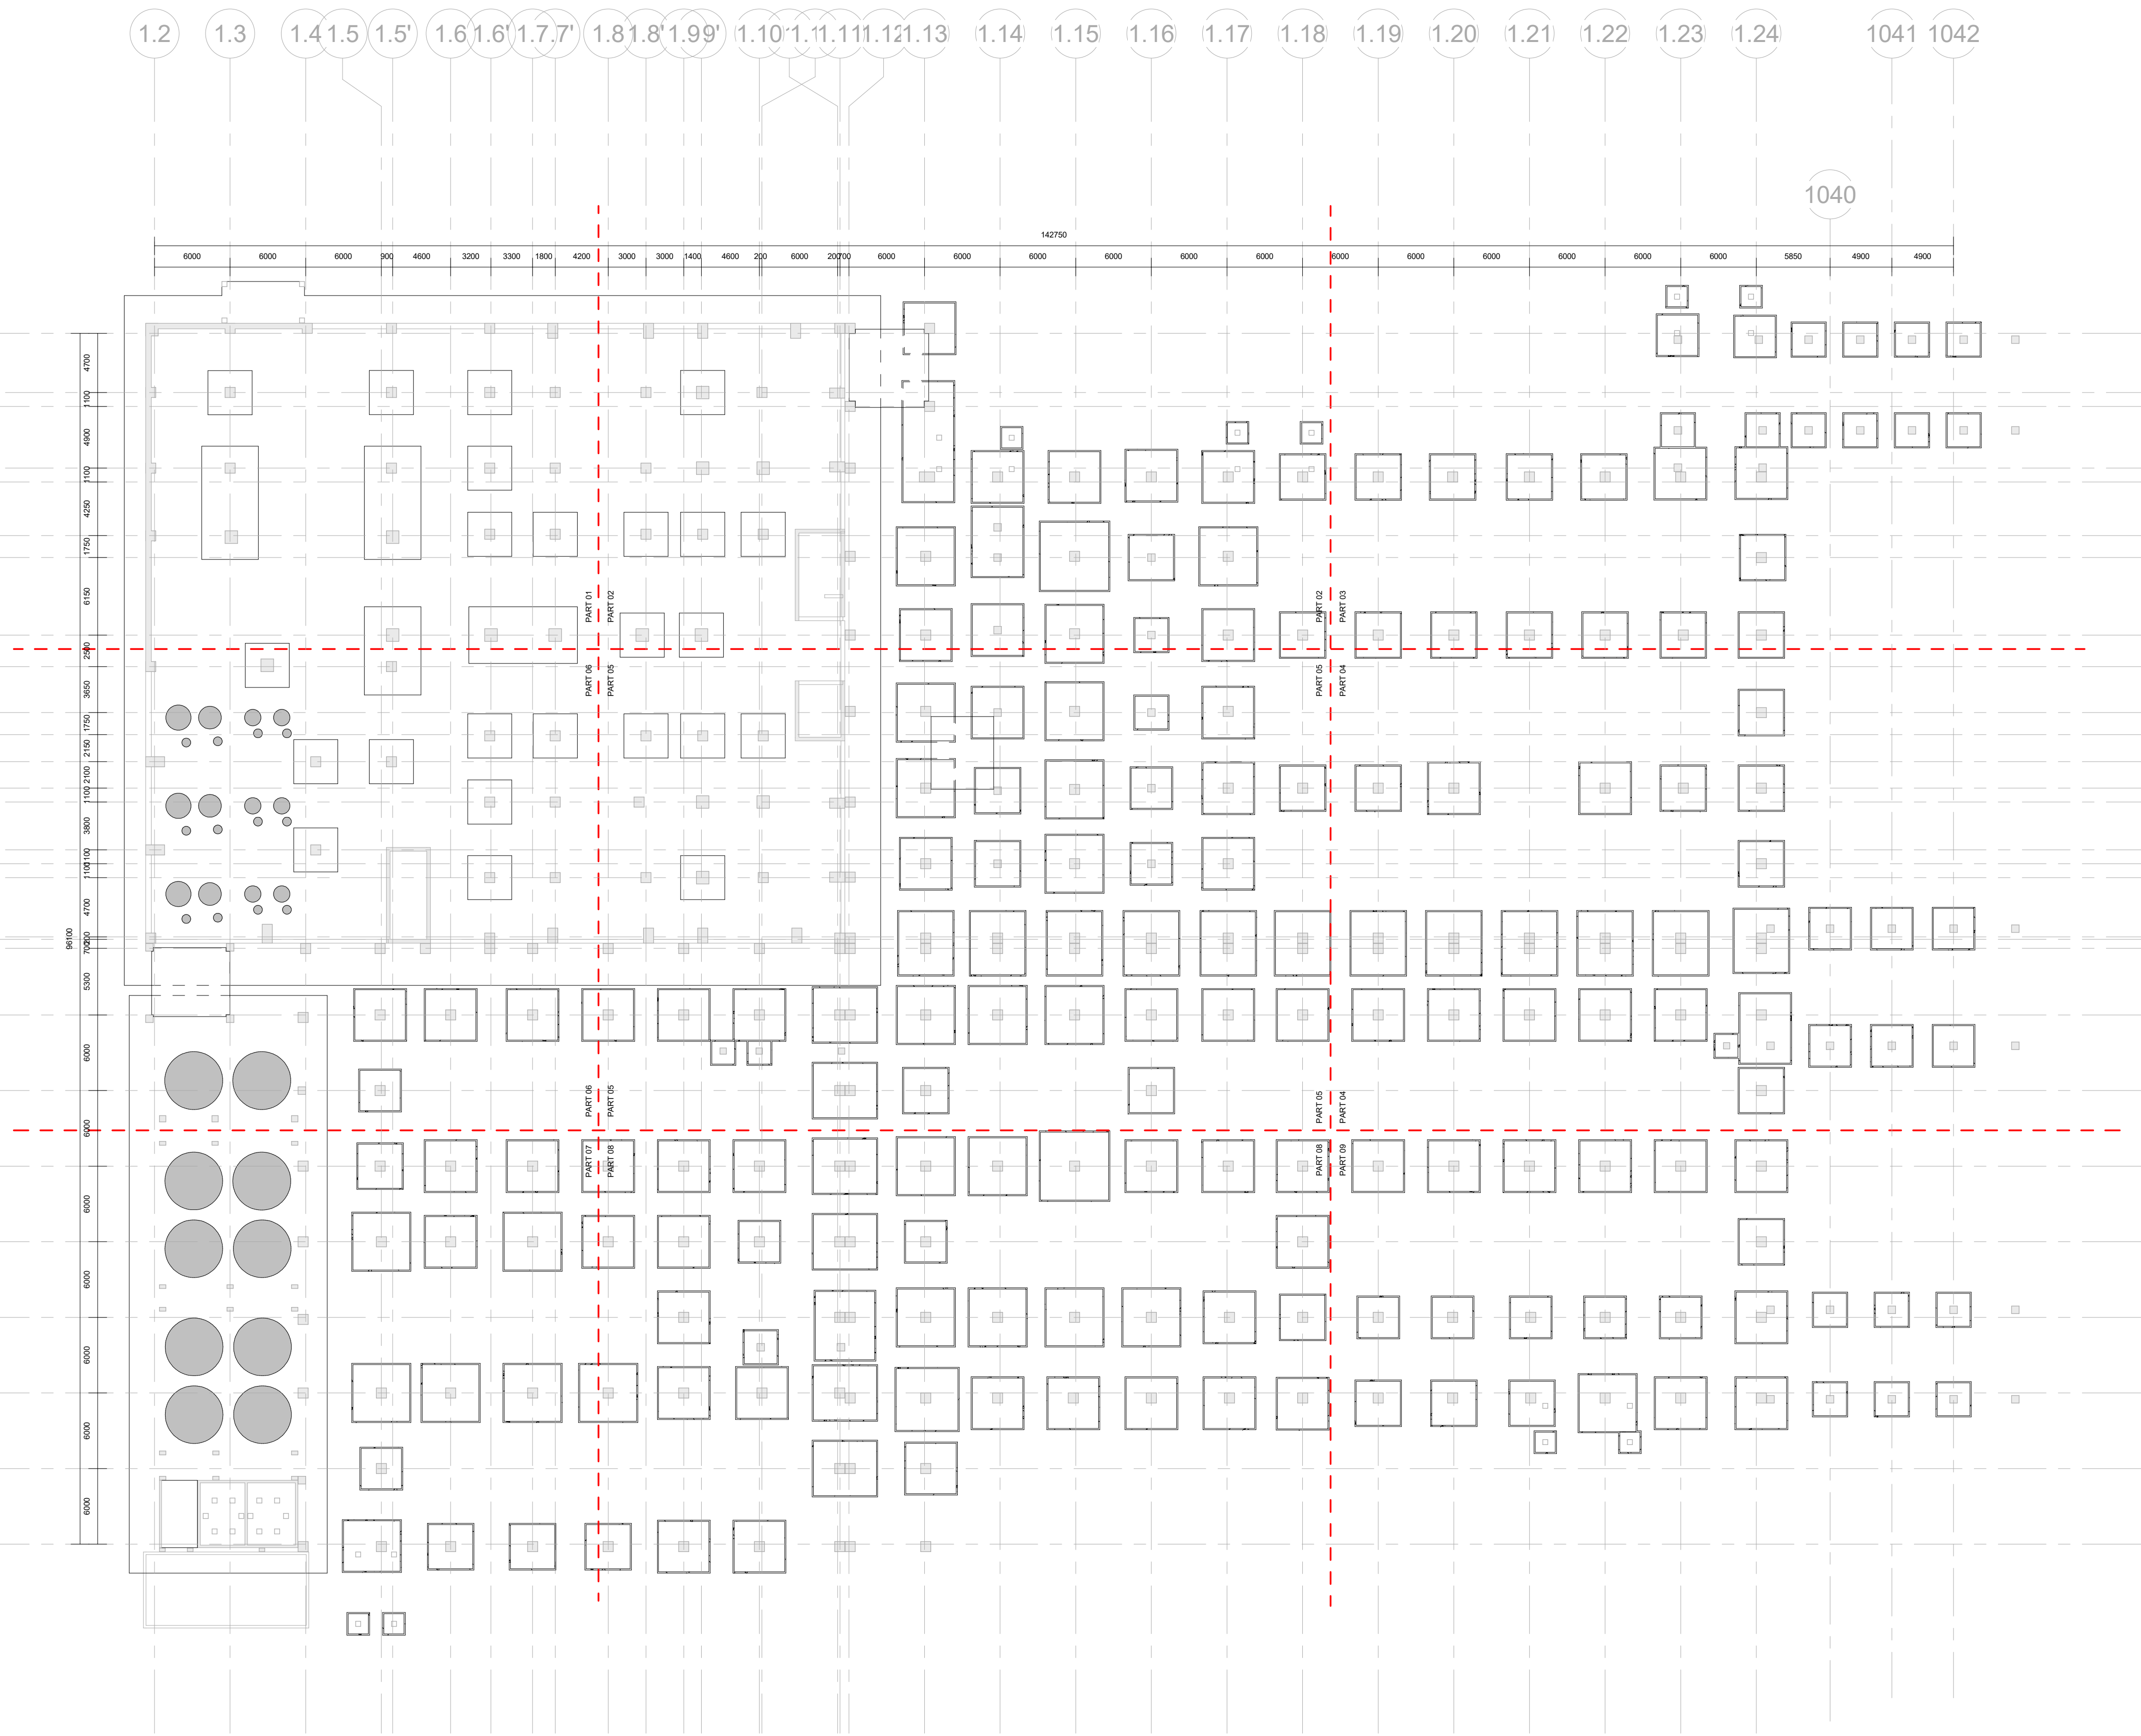


1 FOUNDATION GENERAL ARRANGEMENT OVERALL PLAN
1 : 300

PROJECT NAME AND LOCATION


INTEGRATED DAIRY FRAMING, PRODUCTION AND ARABLE FRAMING
PROJECT - ALGERIA

ADRAR DESERT REGION LOCATED SOUTHERN ALGERIA

NORTH

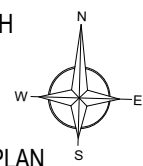

KEY PLAN

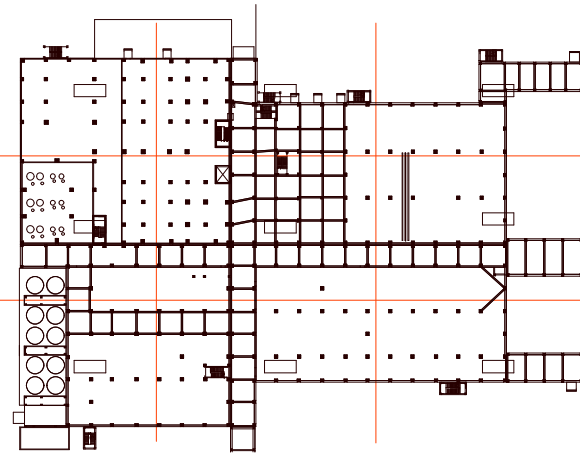

GENERAL NOTES:

1. UNLESS OTHERWISE INDICATED, ALL DIMENSIONS ARE IN MILLIMETERS AND LEVELS IN METERS.
2. ALL DRAWINGS SHALL BE READ IN CONJUNCTION WITH THE RELEVANT ARCHITECTURAL, LANDSCAPE, CIVIL/STRUCTURAL, MECHANICAL AND ELECTRICAL AND TELECOMMUNICATION ENGINEERING DOCUMENTS & PROJECT SPECIFICATIONS.
3. ALL DIMENSIONS ARE TO BE CHECKED AND VERIFIED PRIOR TO THE COMMENCEMENT OF CONSTRUCTION ON SITE. DRAWINGS MUST NOT BE SCALED. ONLY WRITTEN OR CONSOLIDATED DIMENSIONS SHALL BE USED.

REFERENCE DRAWINGS		
DESCRIPTION	DRAWING NO.	REV.
FOUNDATION PLAN OVERALL	BAL-EHF-PD-XXX-DWG-S-XX-10200_02	02

ISSUE FOR APPROVAL				
00	ISSUED FOR APPROVAL	29-06-2026	DRAWN	CHECKED

OWNER

Baladna
Algeria



PM/CM



SUPERVISION CONSULTANT



MANAGING CONTRACTOR



CONTRACTOR

DESIGN CONSULTANT

58 AL-SHOUKHO
TOWERS (TOWER A), 13th
FLOOR OFFICE 184 BIN
MAHMOUD
TEL : (974) 402037 77 / 88 / 99
FAX : (974) 402037 88
P.O. BOX 1676, DOHA-QATAR
www.ehaf.com



ENGINEERING SUBCONTRACTOR

TEL : +962 7 9131 8024
Email: info@eg-consult.com
11118 AMMAN - JORDAN



CONTRACT DESCRIPTION

ALGERIA DAIRY AND ARABLE FARMING
PROJECT

DRAWING TITLE

PRODUCTION BUILDING
FOUNDATION GENERAL
ARRANGEMENT OVERALL PLAN

DRAWING NO.:		PART:	
04A-BA-SDW-ST-P1-MF1-PD-FN-1010-Y00			
DRAWN BY:	CHECK BY:	STAGE:	REVISION:
EG	EG	SD	00
VERIFIED BY:	APPROVED BY:	PLOT DATE:	
		29-06-2026	
SCALE:		CONTRACT NO.:	
1 : 300@A1		04A	
FILE NAME:			
BAL-EHF-PD-ZZZ-MST-ST-ZZ-90100			